


INQUADRAMENTO URBANO (Roma, Villaggio Olimpico, Via Olanda)
SCALA 1:500

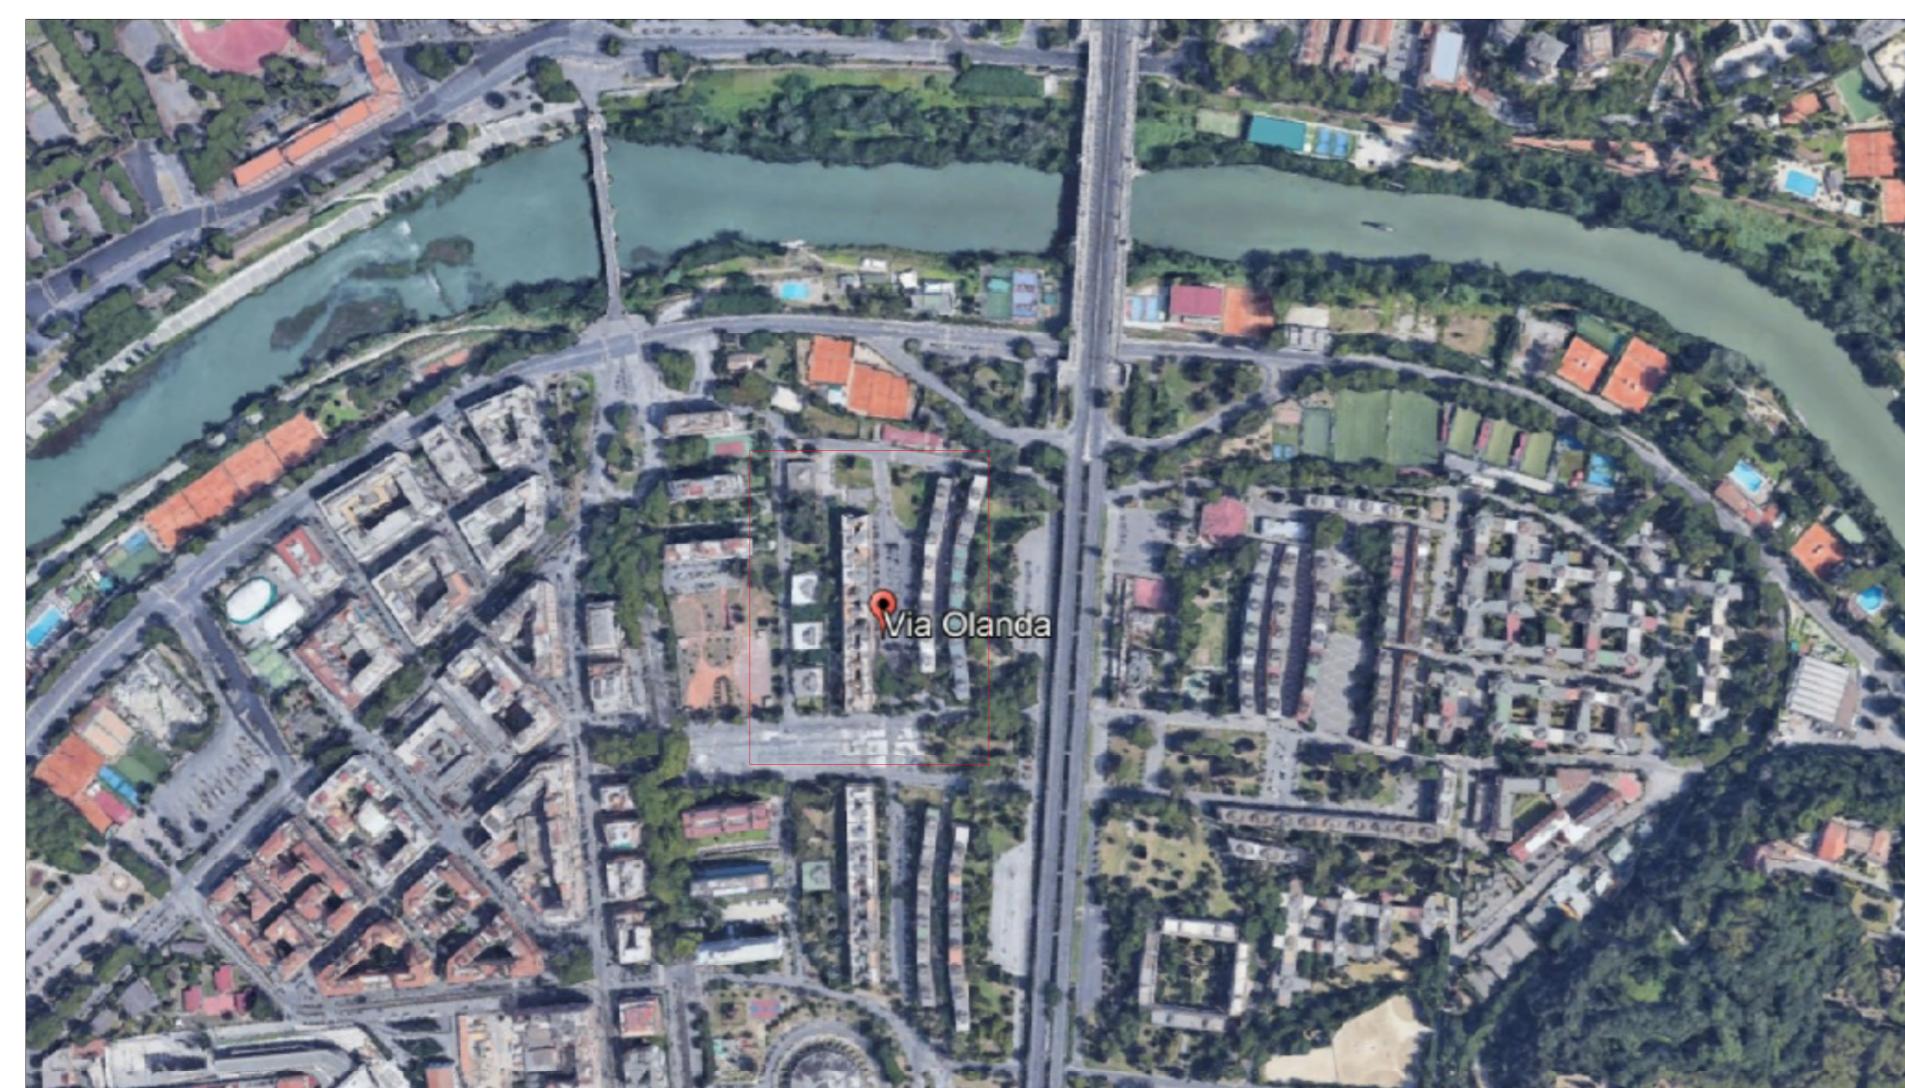


VISTA AEREA
SCALA 1:500



FACCIATA ESISTENTE Rivestimenti in laterizio

PROSPETTO FRONTEALE
Ipotizzando struttura portante rivestimento a cortina in laterizio giallo.
SCALA 1:200

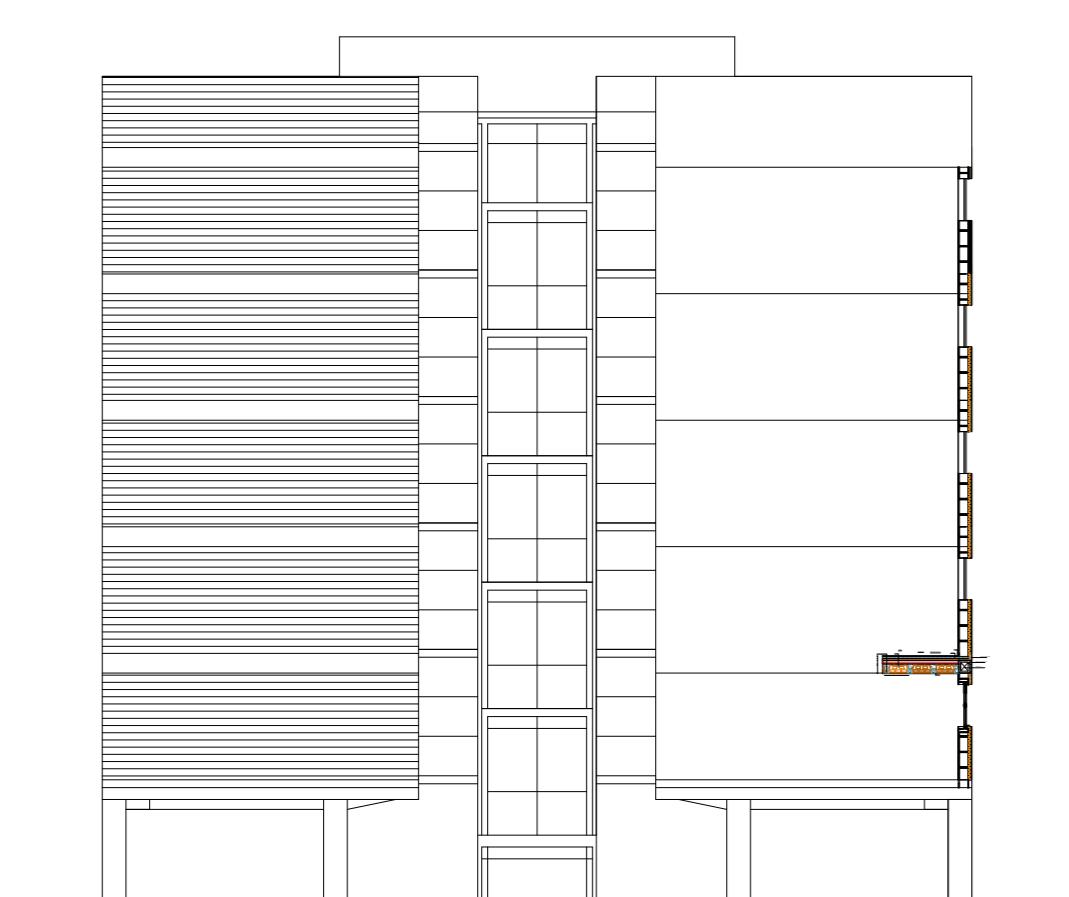


PROSPETTO LATERALE
Finestre a nastro, singole.
SCALA 1:200




RIPENSAMENTO FACCIATA Cappotto esterno


PROSPETTO FRONTEALE
Ipotizzando parete isolata dall'esterno con lastre di PVC
SCALA 1:200

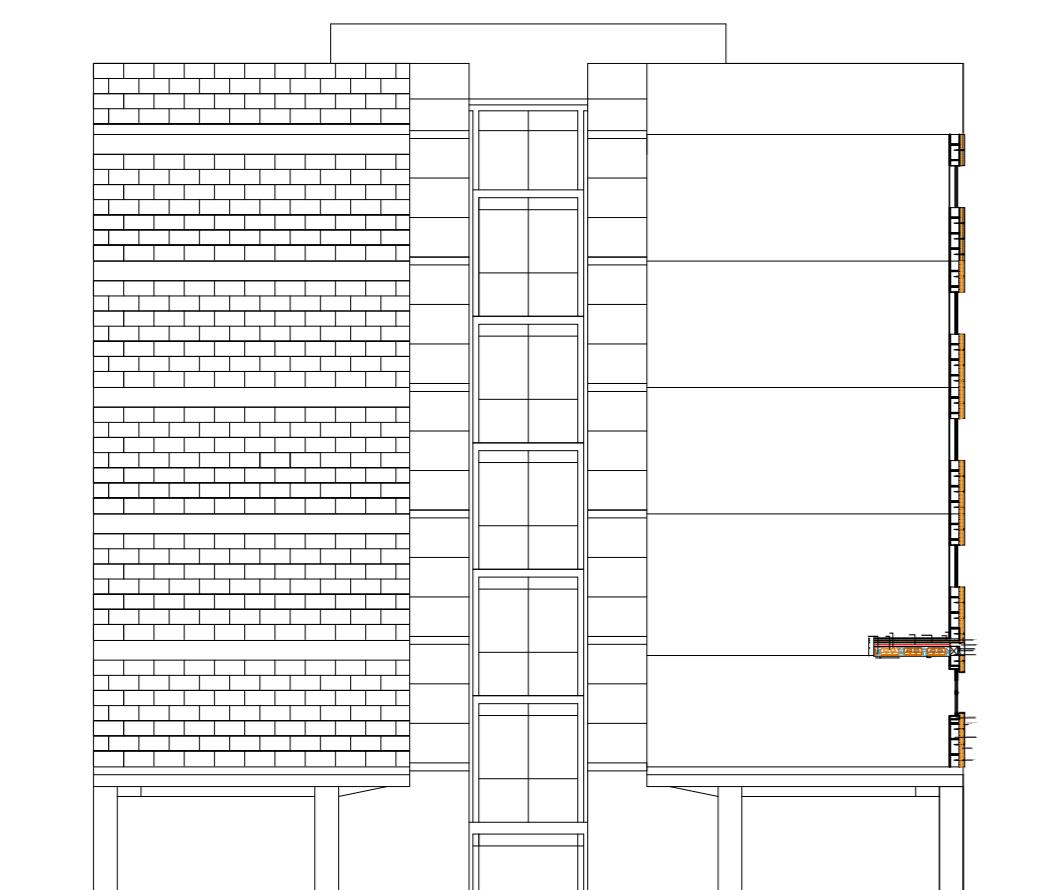


PROSPETTO LATERALE
Finestre a nastro unite.
SCALA 1:200

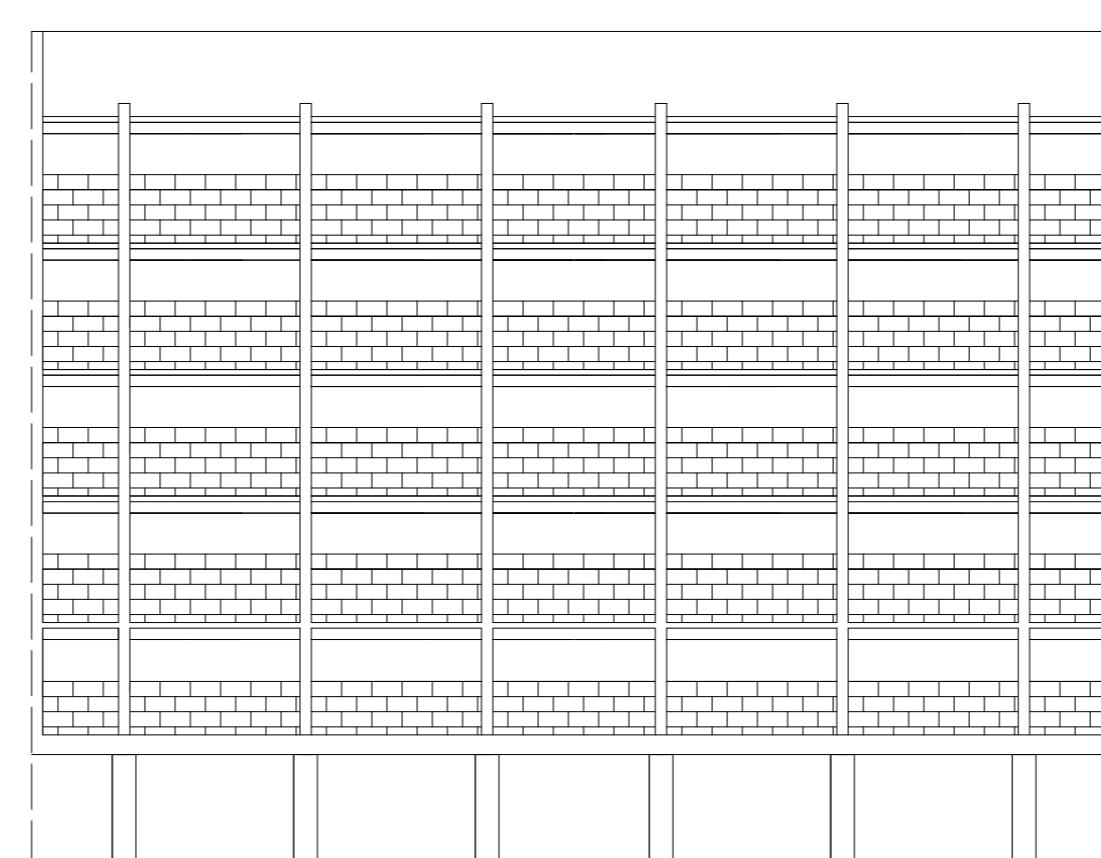

SEZIONE MURO PERIMETRALE
SCALA 1:20

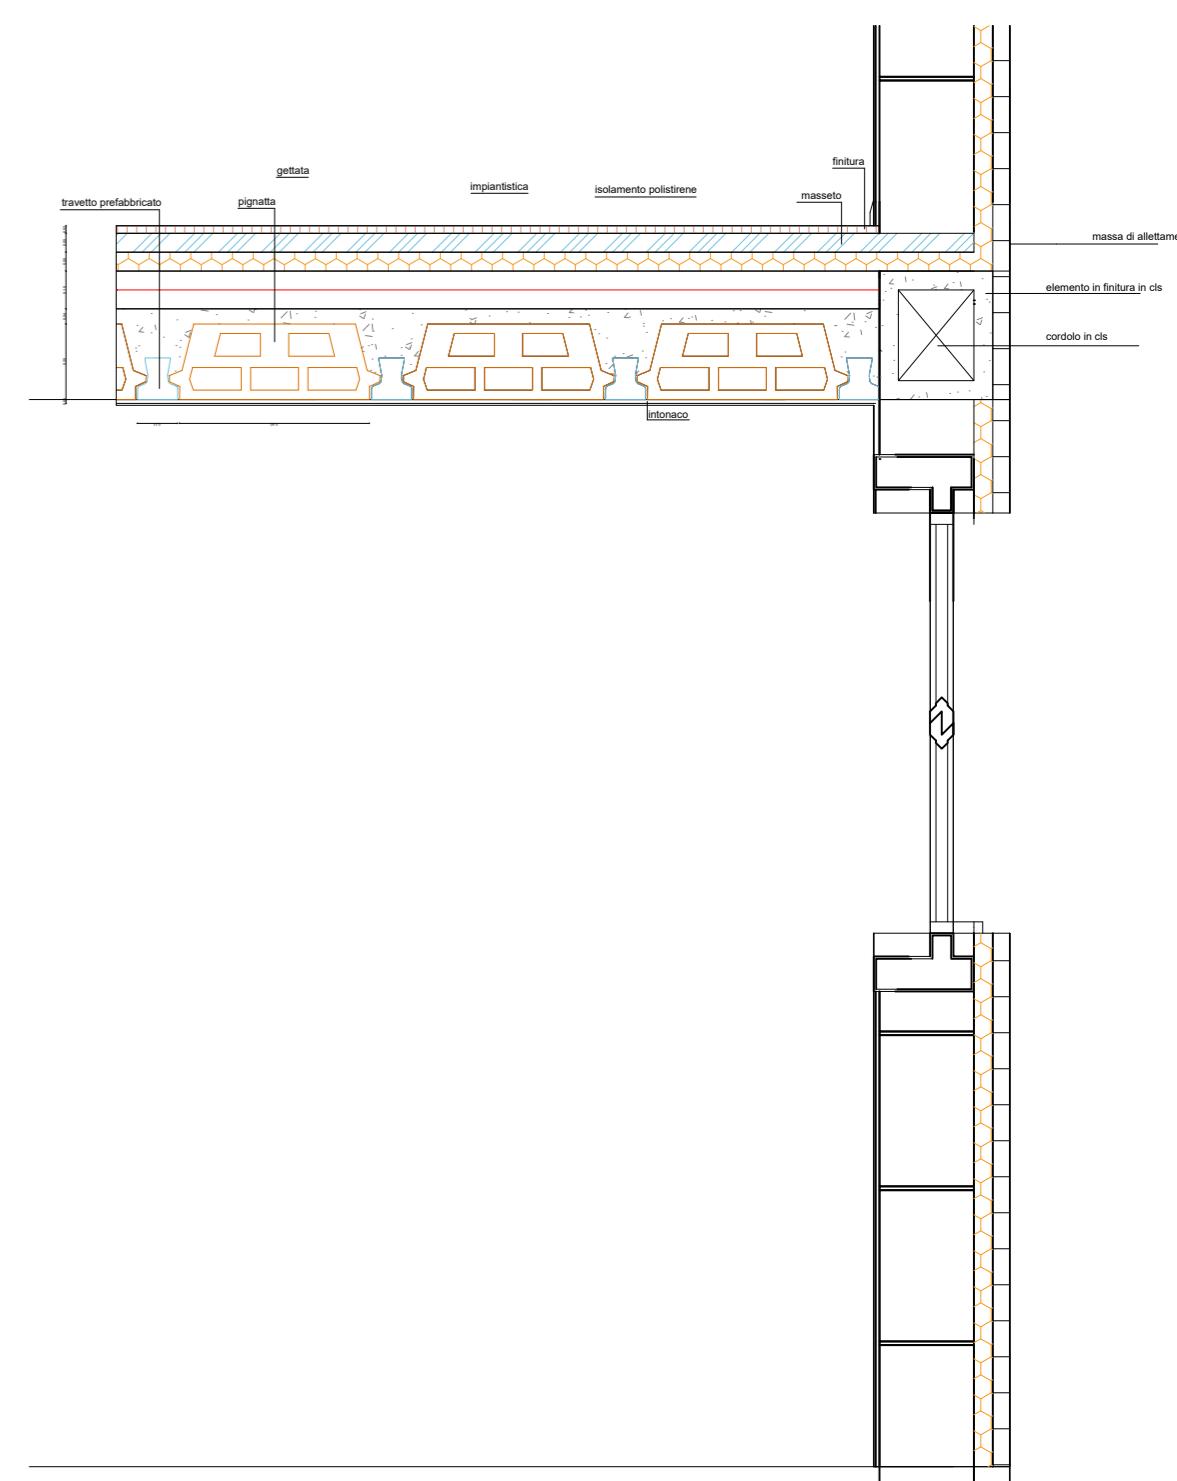

SEZIONE MURO PERIMETRALE
SCALA 1:20

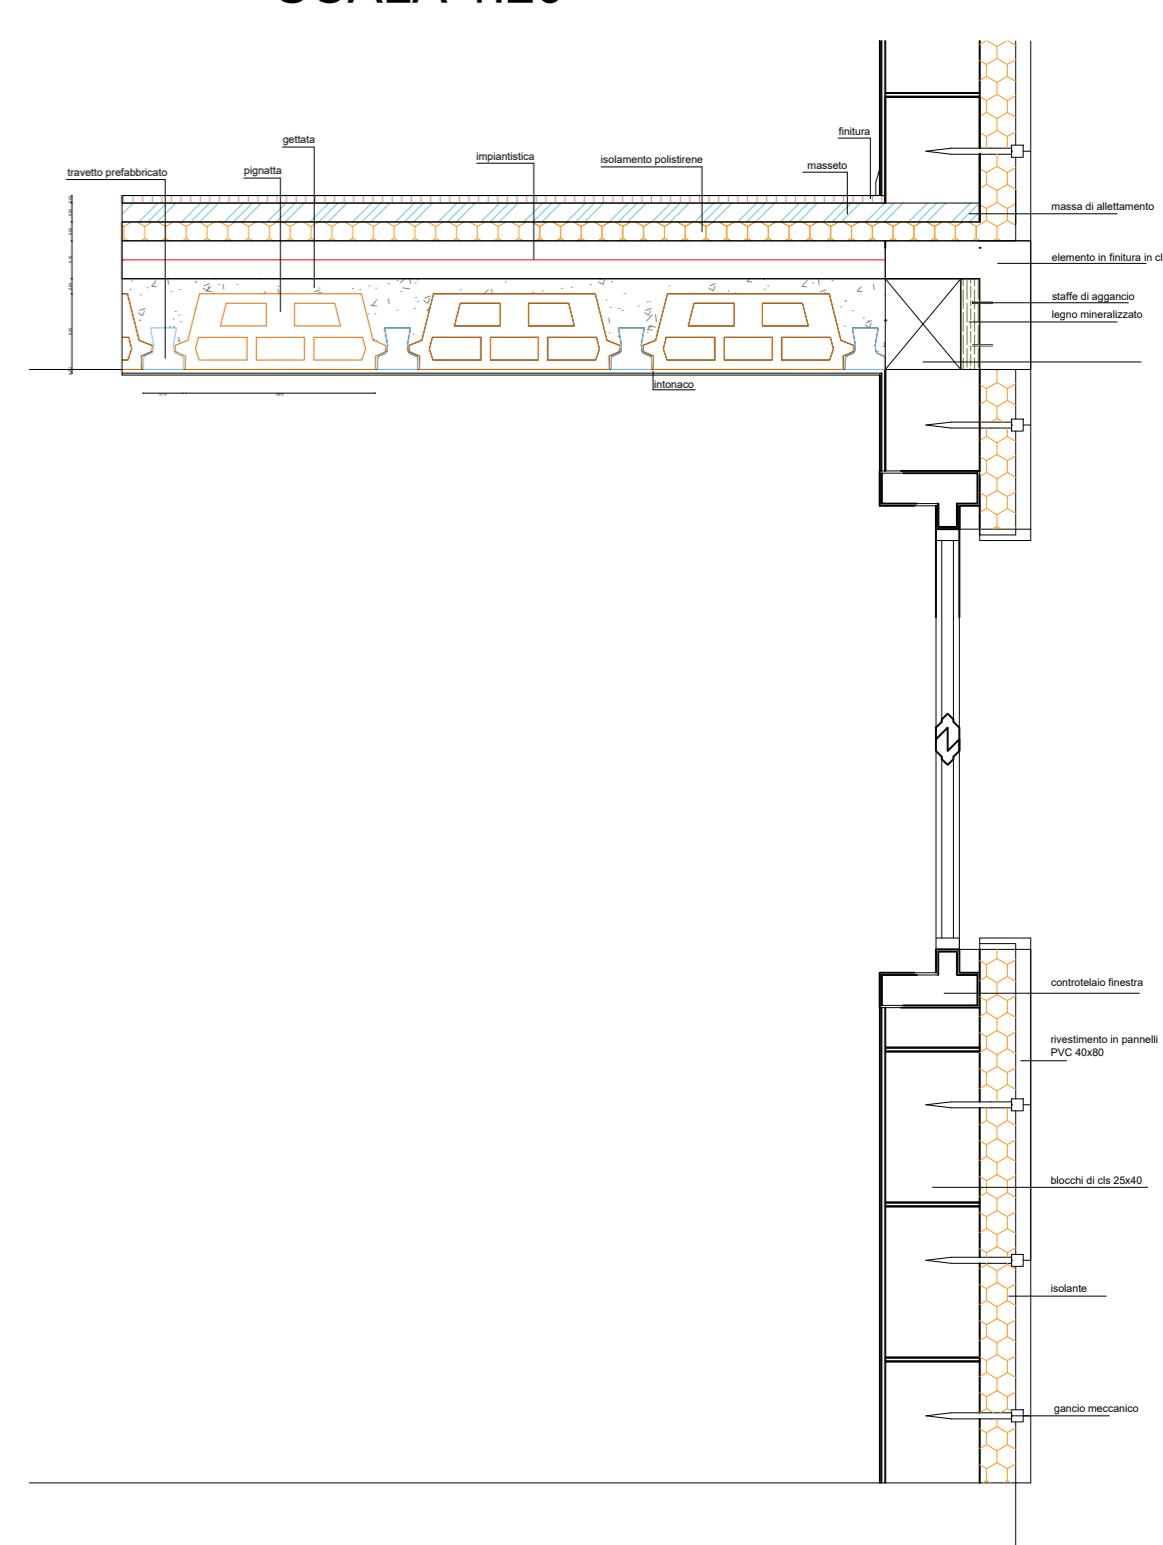

| FACCIATA ESISTENTE: struttura portante | RIPENSAMENTO FACCIATA: cappotto esterno (vetture) |
|--|---|
| Portante e Non | Portante e Non |
| Realizzazione semplice | Realizzazione complessa |
| Composta da piccoli elementi artificiali (laterizio) | Composta da piccoli elementi prefabbricati |
| Poco isolata (termico, acustico) | Isolata (rinnovamento termico e acustico) |
| Resistenza meccanica scarsa | Resistenza meccanica buona |
| Resistenza a fuoco | Resistenza a fuoco |
| Bassa durabilità | Riqualifica e più durabile |
| Da riqualificare | Riqualifica |

